
Proj. kabel Z-XOTksd - WTROI/121850000000339/AA
dł. trasowa w kanalizacji Orange Polska S.A.: 1153,4 m
dł. montażowa w kanalizacji Orange Polska S.A.: 1290,0 m

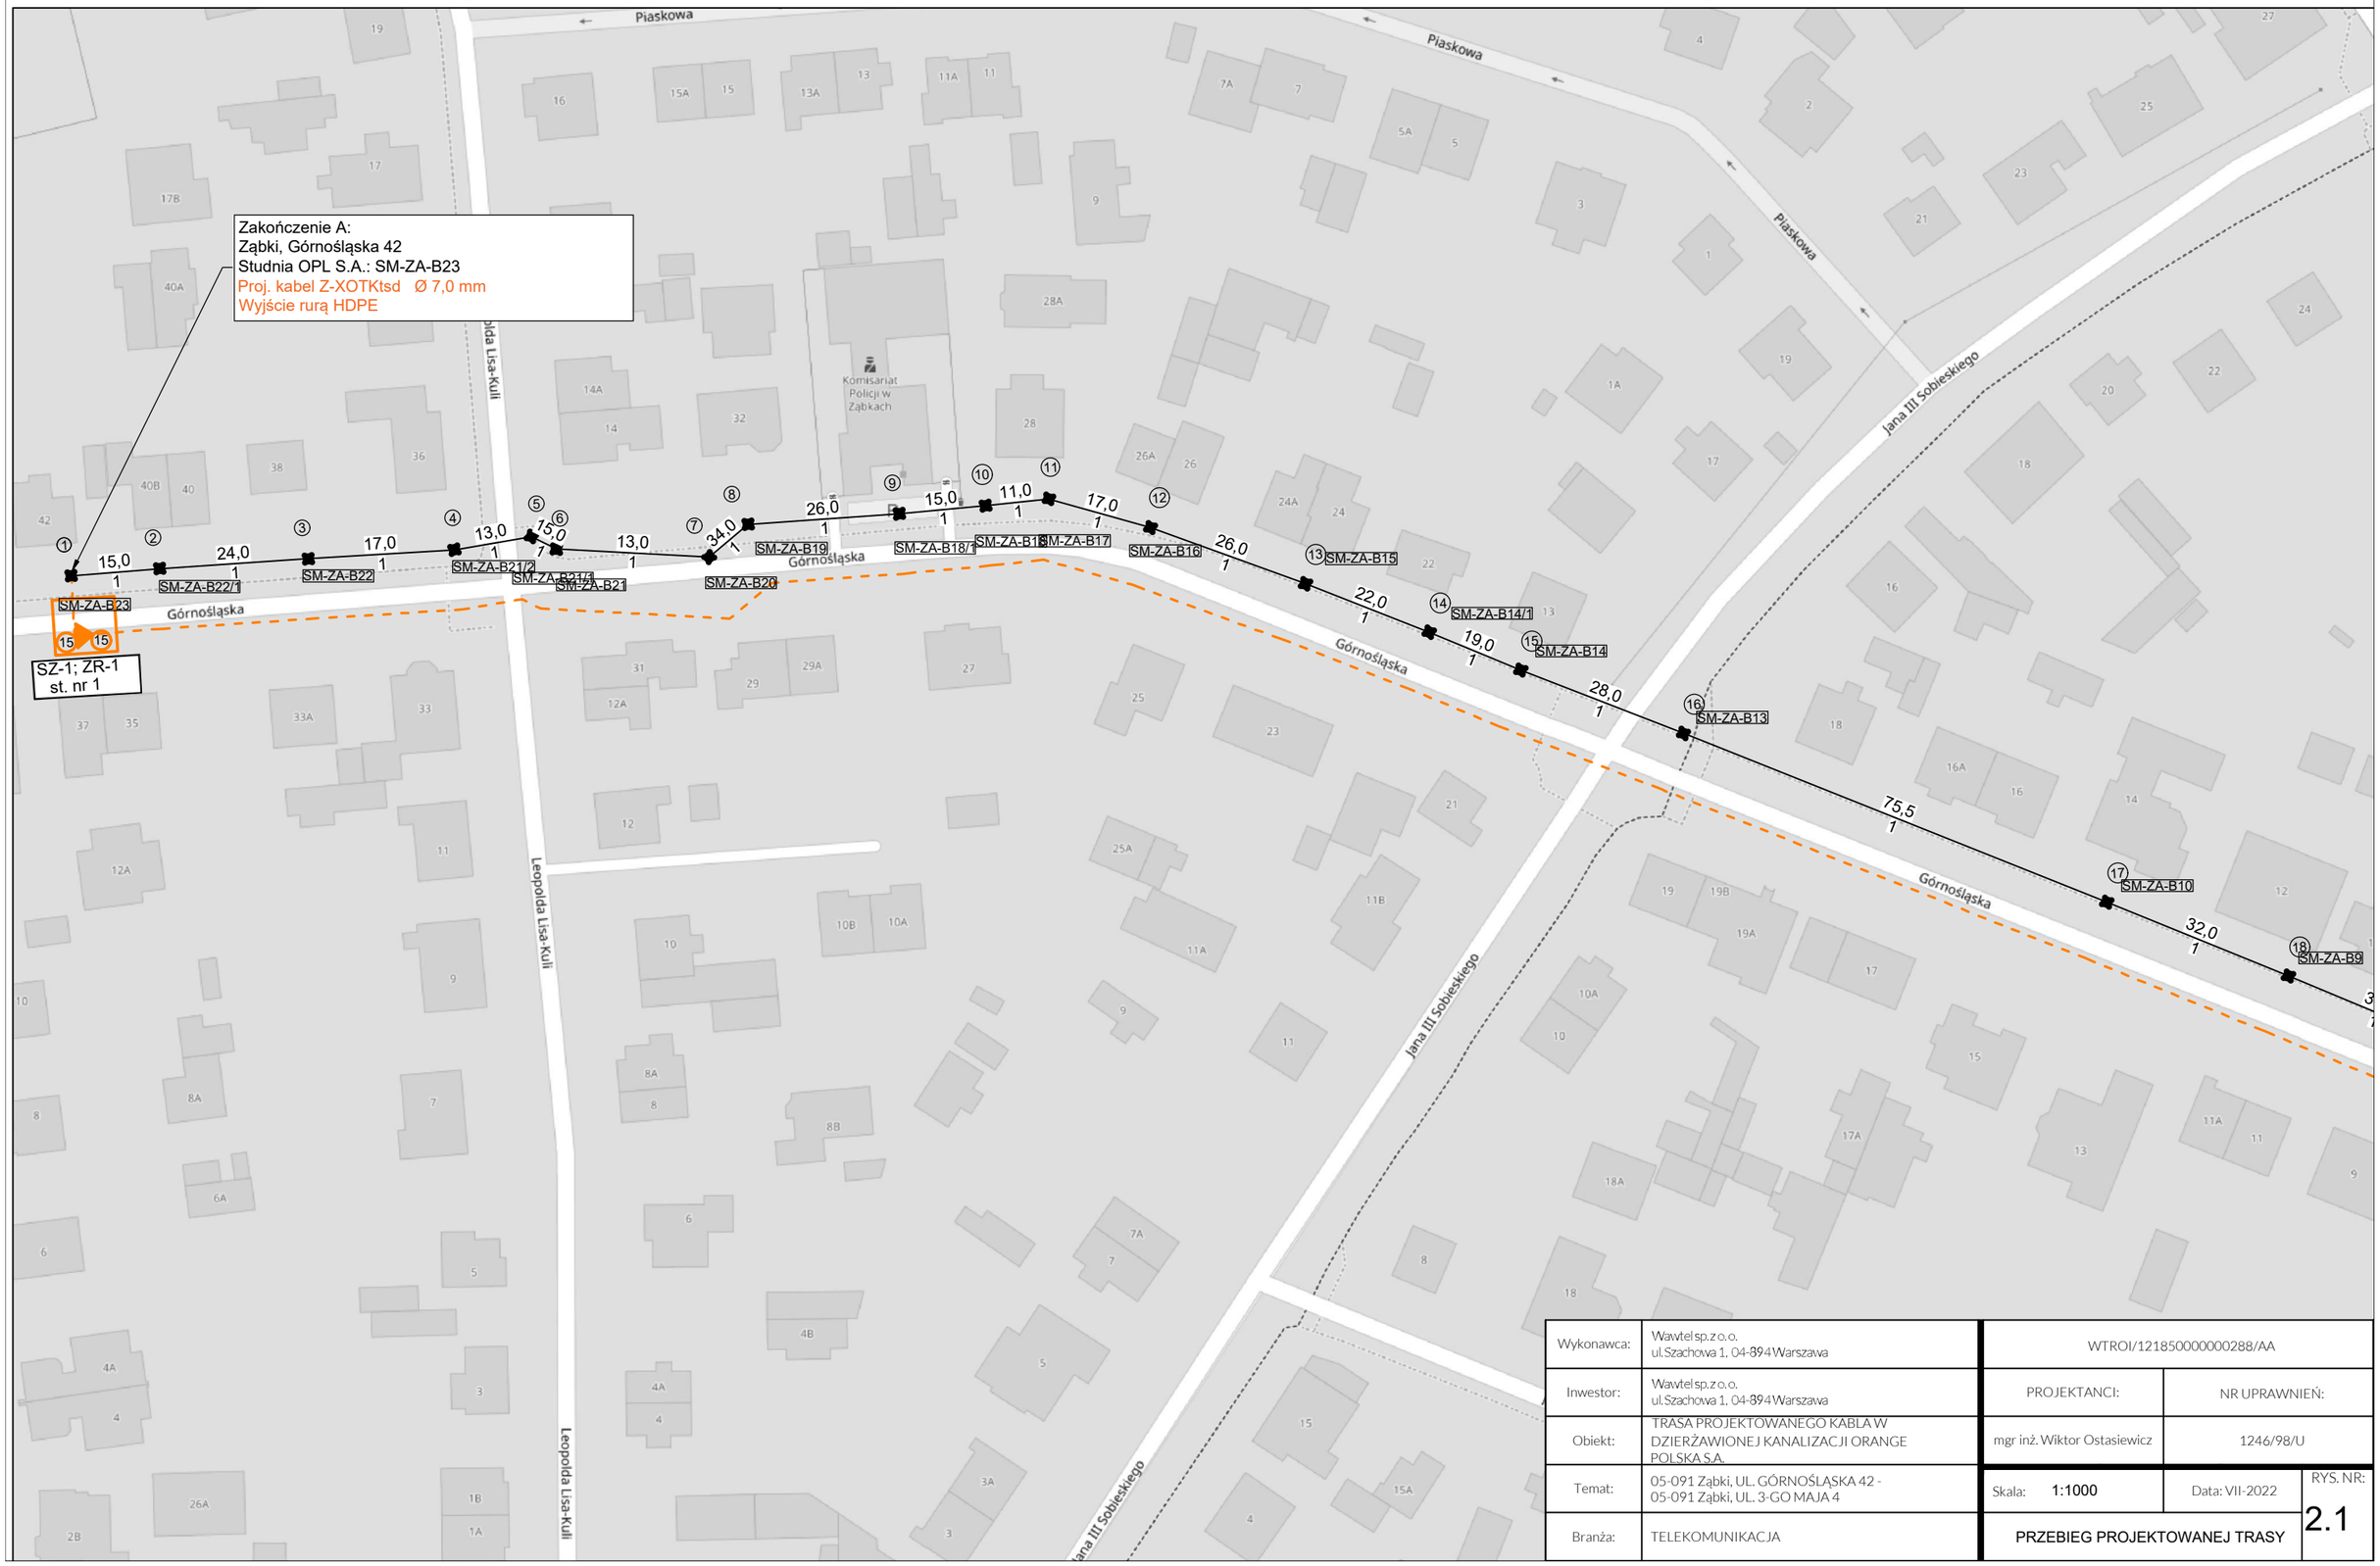

Wykonawca:	Wawtel sp. z o.o. ul. Szachowa 1, 04-894 Warszawa	WTROI/121850000000288/AA	
Inwestor:	Wawtel sp. z o.o. ul. Szachowa 1, 04-894 Warszawa	PROJEKTANCI:	NR UPRAWNIEŃ:
Obiekt:	TRASA PROJEKTOWANEGO KABLA W DZIERŻAWIONEJ KANALIZACJI ORANGE POLSKA S.A.	mgr inż. Wiktor Ostasiewicz	1246/98/U
Temat:	05-091 Ząbki, UL. GÓRNOŚLĄSKA 42 - 05-091 Ząbki, UL. 3-GO MAJA 4	Skala: 1:1000	Data: VII-2022
Branża:	TELEKOMUNIKACJA	PRZEBIEG PROJEKTOWANEJ TRASY	RYS. NR: 2.1

Proj. kabel Z-XOTksd - WTROI/121850000000339/AA
dł. trasowa w kanalizacji Orange Polska S.A.: 1153,4 m
dł. montażowa w kanalizacji Orange Polska S.A.: 1290,0 m

SM-ZA-B10 — 32,0 / 1 — SM-ZA-B9 — 31,0 / 1 — SM-ZA-B8 — 42,0 / 1 — SM-ZA-B7 — 37,0 / 1 — SM-ZA-B6 — 14,5 / 1 — SM-ZA-B5/1 — 33,0 / 1 — SM-ZA-B5 — 19,0 / 1 — SM-ZA-B4 — 19,0 / 1 — SM-ZA-B3 — 37,0 / 1 — SM-ZA-B2 — 2,5 / 1 — SM-ZA-B2/1 — 14,0 / 1 — SM-ZA-B1 — 69,0 / 1 — SM-ZA-A3 — 2,0 / 1 — SM-ZA-A4 — 54,5 / 1 — SM-ZA-A5 — 42,0 / 1 — SM-ZA-A6/1

SZ-2; ZR-2 st. nr 22

Górnośląska
Wojska Polskiego
Jana Paderewskiego
Cypriana Kamila Norwida
Stanisława Moniuszki
Marii Konopnickiej
Doktora Adama Leszyckiego
Stefana Batorego
Brama Niepodległości
Flo-Dental
U CHŁOPAKÓW Pizza & Food
Darnell Butik
Urząd Miasta Ząbki
Centrum Obsługi Prawnej Probitas
Forpiyt
Flash Foto Jola
Apteka E. Kopczyńskiej
Leszyckiego 01
3A Blok 1
3B Blok 2
3C Blok 3
3D Blok 4
Blok 5
Blok 6
Urząd Miasta 01

Wykonawca:	Wawtel sp. z o.o. ul. Szachowa 1, 04-894 Warszawa	WTROI/121850000000288/AA	
Inwestor:	Wawtel sp. z o.o. ul. Szachowa 1, 04-894 Warszawa	PROJEKTANCI:	NR UPRAWNIEŃ:
Obiekt:	TRASA PROJEKTOWANEGO KABLA W DZIERŻAWIONEJ KANALIZACJI ORANGE POLSKA S.A.	mgr inż. Wiktor Ostasiewicz	1246/98/U
Temat:	05-091 Ząbki, UL. GÓRNOŚLĄSKA 42 - 05-091 Ząbki, UL. 3-GO MAJA 4	Skala: 1:1000	Data: VII-2022
Branża:	TELEKOMUNIKACJA	PRZEBIEG PROJEKTOWANEJ TRASY	RYS. NR: 2.2

Proj. kabel Z-XOTksd - WTROI/121850000000339/AA
dł. trasowa w kanalizacji Orange Polska S.A.: 1153,4 m
dł. montażowa w kanalizacji Orange Polska S.A.: 1290,0 m

SM-ZA-A6/1
SM-ZA-A6/2
SM-ZA-A7
SM-ZA-A8
SM-ZA-A9
SM-ZA-A10
SM-ZA-A11
SM-ZA-A13
SM-ZA-A14
SM-ZA-A14/1

42,0 1
38,2 1
50,7 1
58,0 1
53,0 1
54,5 1
13,0 1
41,0 1
11,5 1
14,5 1

SZ-8: ZR-3 st. nr 40

Zakończenie B:
Ząbki, 3 Maja 4
Studnia OPL S.A.: SM-ZA-A14/1
Proj. kabel Z-XOTKtsd Ø 7,0 mm
Dowiązanie do projektowanej mufy

Wykonawca:	Wawtel sp.z o.o. ul.Szachowa 1, 04-894 Warszawa	WTROI/121850000000288/AA	
Inwestor:	Wawtel sp.z o.o. ul.Szachowa 1, 04-894 Warszawa	PROJEKTANCI:	NR UPRAWNIEŃ:
Obiekt:	TRASA PROJEKTOWANEGO KABLA W DZIERŻAWIONEJ KANALIZACJI ORANGE POLSKA S.A.	mgr inż. Wiktor Ostasiewicz	1246/98/U
Temat:	05-091 Ząbki, UL. GÓRNOŚLĄSKA 42 - 05-091 Ząbki, UL. 3-GO MAJA 4	Skala: 1:1000 / Data: VII-2022	RYS. NR: 2.2
Branża:	TELEKOMUNIKACJA	PRZEBIEG PROJEKTOWANEJ TRASY	